
# DJ-CF-01 | EXISTING PLAN

## 직장인 생활권 소형 카페 고객공간 리뉴얼

교육용 기준 평면도 · 개정 02 · 실제 실측도면 또는 법적 도면이 아님

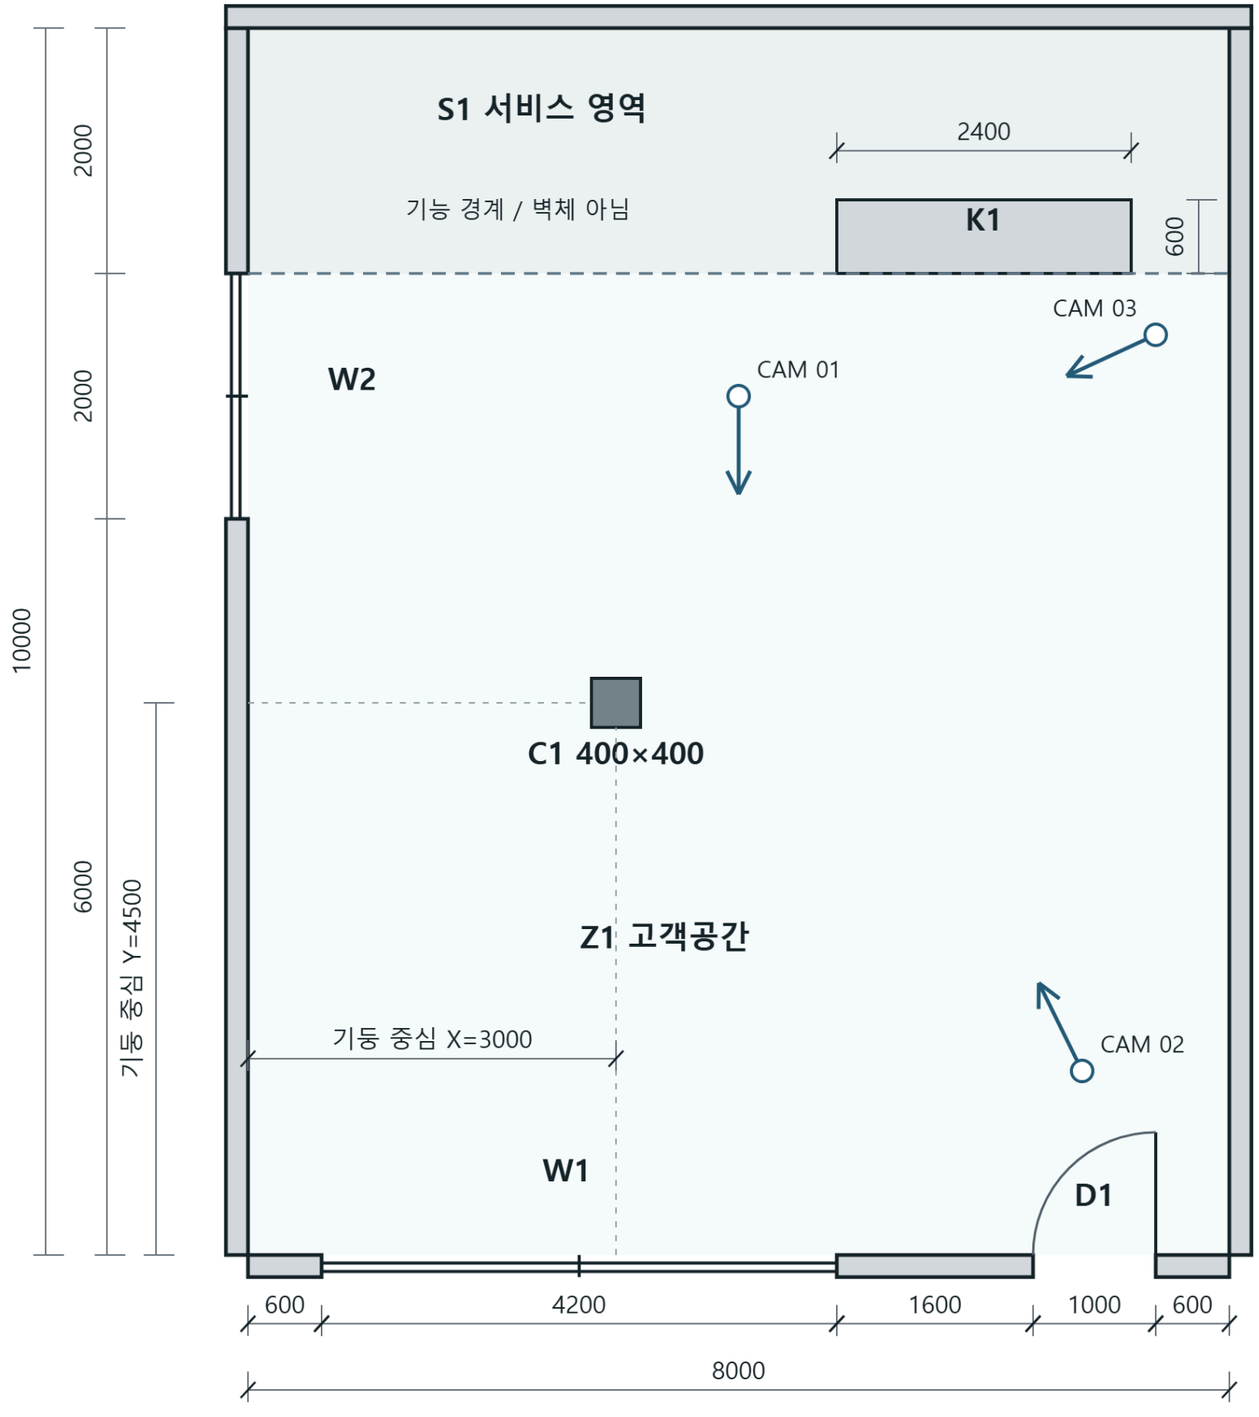


N

### 도면 읽기

**01 유지 요소**

D1 · W1 · W2 · C1 · K1 · S1 유지

**02 변경 가능한 영역**

Z1의 이동식 가구 / 마감 색감 / 조명 표현

**03 서비스 영역**

S1의 점선은 기능 구분선이며 벽체가 아님

**04 개구부 높이**

D1: H2200 / W1: 하단600~상단2400

W2: 하단900~상단2200

**05 공간 조건**

천장 H3000 / 기준 영역 80㎡

벽 두께 180은 시각화용 설정, 구조 판단 불가

**06 카메라**

01 남측 / 02 북서측 / 03 남서측

눈높이 1500 / 기준 화각 28mm

**07 과제 범위**

12~16석은 교육용 목표, 법적 수용인원 아님

완성 가구 배치 정답은 포함하지 않음

범례: 굵은 실선 = 기존 벽체 / 회색 = 고정 요소

점선 = 기능 경계 / 파란 화살표 = 카메라 방향

0 1 2 3 4m

A3 · 1:50 @ 100% · 단위 mm · 남서 실내 모서리 원점 · DJ-CF-01