서산테크노밸리 조 성 사 업 지구단위계획

건축물 등에 관한 도시관리계획 결정도



범 례

- 지구단위계획구역
- 획지경계선
- 대지분할가능선
- 건축한계선(m)
- 벽면한계선(m)(8층이상)
- 25층이하
- 20층이하
- 12층이하
- 차량출입구(권장)
- 주동방향
- 연도형상가(권장)
- 경관지표등(권장)
- 보행자전용도로
- 단지내 보행통로
- 공공보행통로
- 차량출입불허구간

※ 공동주택용지

용도	용적률(%이하) (기준/허용/상한)	최고층수(층이하) (권고층수(층이하))
	건폐율(%이하)	-

※ 산업시설용지

용도	용적률(%이하)	최고층수(층이하)
	건폐율(%이하) (기준/허용)	-

※ 기타시설용지

용도	용적률(%이하)	최고층수(층이하)
	건폐율(%이하)	최저층수(층이상)


N

SCALE : 1/2,000

0 25 50 100(m)

서산테크노밸리 조성사업 지구단위계획

건축물 등에 관한 도시관리계획 결정도

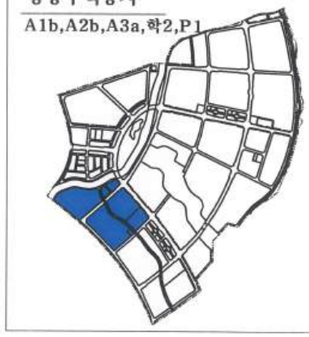

범 례

- 지구단위계획구역
- 획지경계선
- 대지분할가능선
- 건축한계선(m)
- 벽면한계선(m)(8층이상)
- 25층이하
- 20층이하
- 12층이하
- 차량출입구(권장)
- 주동방향
- 연도형상가(권장)
- 경관지표등(권장)
- 보행자전용도로
- 단지내 보행통로
- 공공보행통로
- 차량출입불허구간

※ 공동주택용지

용도		
	용적률(%이하) (기준/허용/상한)	최고층수(층이하) (평균층수(층이하))
	건폐율(%이하)	-

※ 산업시설용지

용도		
	용적률(%이하)	최고층수(층이하)
	건폐율(%이하) (기준/완화)	-

※ 기타시설용지

용도		
	용적률(%이하)	최고층수(층이하)
	건폐율(%이하)	최저층수(층이상)

N

SCALE : 1/2,000

0 25 50 100(m)

서산테크노밸리 조성사업 지구단위계획

건축물 등에 관한 도시관리계획 결정도



범 례

- 지구단위계획구역
- 획지경계선
- 대지분할가능선
- 건축한계선(m)
- 벽면한계선(m)(8층이상)
- 25층이하
- 20층이하
- 12층이하
- 차량출입구(권장)
- 주동방향
- 연도형상가(권장)
- 경관지표등(권장)
- 보행자전용도로
- 단지내 보행통로
- 공공보행통로
- 차량출입불허구간

※ 공동주택용지

용도	용적률(%이하) (기준/최대/상한)	최고층수(층이하) (평균층수(층이하))
	건폐율(%이하)	-

※ 산업시설용지

용도	용적률(%이하)	최고층수(층이하)
	건폐율(%이하) (기준/완화)	-

※ 기타시설용지

용도	용적률(%이하)	최고층수(층이하)
	건폐율(%이하)	최저층수(층이상)

SCALE : 1/2,000

0 25 50 100(m)

서산테크노밸리 조성사업 지구단위계획

건축물 등에 관한 도시관리계획 결정도



범 례

- 지구단위계획구역
- 획지경계선
- 대지분할가능선
- 건축한계선(m)
- 벽면한계선(m)(8층이상)
- 25층이하
- 20층이하
- 12층이하
- 차량출입구(권장)
- 주동방향
- 연도형상가(권장)
- 경관지표등(권장)
- 보행자전용도로
- 단지내 보행통로
- 공공보행통로
- 차량출입불허구간

※ 공동주택용지

용도	용적률(%이하) (기준/최종/상한)	최고층수(층이하) (평균층수(층이하))
	건폐율(%이하)	-

※ 산업시설용지

용도	용적률(%이하)	최고층수(층이하)
	건폐율(%이하) (기준/완화)	-

※ 기타시설용지

용도	용적률(%이하)	최고층수(층이하)
	건폐율(%이하)	최저층수(층이상)


N

SCALE : 1/2,000

0 25 50 100(m)

서산테크노밸리 조성사업 지구단위계획

건축물 등에 관한 도시관리계획 결정도

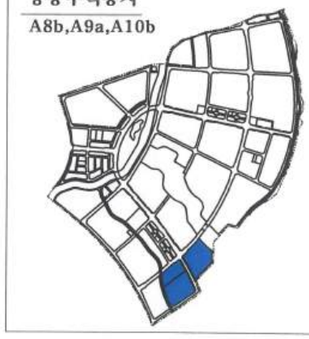

범 례

- 지구단위계획구역
- 획지경계선
- 대지분할가능선
- 건축한계선(m)
- 벽면한계선(m)(8층이상)
- 25층이하
- 20층이하
- 12층이하
- 차량출입구(권장)
- 주동방향
- 연도형상가(권장)
- 경관지표등(권장)
- 보행자전용도로
- 단지내 보행통로
- 공공보행통로
- 차량출입불허구간

※ 공동주택용지

용도	용적률(%이하) (기준/최대/상한)	최고층수(층이하) (평균층수(층이하))
	건폐율(%이하)	-

※ 산업시설용지

용도	용적률(%이하)	최고층수(층이하)
	건폐율(%이하) (기준/완화)	-

※ 기타시설용지

용도	용적률(%이하)	최고층수(층이하)
	건폐율(%이하)	최저층수(층이상)

N

SCALE : 1/2,000

0 25 50 100(m)

서산테크노밸리 조성사업 지구단위계획

건축물 등에 관한 도시관리계획 결정도



범 례

- 지구단위계획구역
- 획지경계선
- 대지분할가능선
- 건축한계선(m)
- 벽면한계선(m)(8층이상)
- 25층이하
- 20층이하
- 12층이하
- 차량출입구(권장)
- 주동방향
- 연도형상가(권장)
- 경관지표등(권장)
- 보행자전용도로
- 단지내 보행통로
- 공공보행통로
- 차량출입불허구간

※ 공동주택용지

용도	용적률(%이하) (기준/허용/상한)	최고층수(층이하) (평균층수(층이하))
	건폐율(%이하)	-

※ 산업시설용지

용도	용적률(%이하)	최고층수(층이하)
	건폐율(%이하) (기준/완화)	-

※ 기타시설용지

용도	용적률(%이하)	최고층수(층이하)
	건폐율(%이하)	최저층수(층이상)

N

SCALE : 1/2,000

0 25 50 100(m)

서산테크노밸리 조성사업 지구단위계획

건축물 등에 관한 도시관리계획 결정도



범 례

- 지구단위계획구역
- 획지경계선
- 대지분할가능선
- 건축한계선(m)
- 벽면한계선(m)(8층이상)
- 25층이하
- 20층이하
- 12층이하
- 차량출입구(권장)
- 주동방향
- 연도형상가(권장)
- 경관지표등(권장)
- 보행자전용도로
- 단지내 보행통로
- 공공보행통로
- 차량출입불허구간

※ 공동주택용지

용도	용적률(%이하) (기준/허용/상한)	최고층수(층이하) (평균층수(층이하))
	건폐율(%이하)	-

※ 산업시설용지

용도	용적률(%이하)	최고층수(층이하)
	건폐율(%이하) (기준/완화)	-

※ 기타시설용지

용도	용적률(%이하)	최고층수(층이하)
	건폐율(%이하)	최저층수(층이상)

N

SCALE : 1/2,000

0 25 50 100(m)

서산테크노밸리 조 성 사 업 지구단위계획

건축물 등에 관한 도시관리계획 결정도



범 례

- 지구단위계획구역
- 획지경계선
- 대지분할가능선
- 건축한계선(m)
- 벽면한계선(m)(8층이상)
- 25층이하
- 20층이하
- 12층이하
- 차량출입구(권장)
- 주통방향
- 연도형상가(권장)
- 경관지표등(권장)
- 보행자전용도로
- 단지내 보행통로
- 공공보행통로
- 차량출입불허구간

※ 공동주택용지

용도	용적률(%이하) (기준/최통/상한)	최고층수(층이하) (평균층수(층이하))
	건폐율(%이하)	-

※ 산업시설용지

용도	용적률(%이하)	최고층수(층이하)
	건폐율(%이하) (기준/완화)	-

※ 기타시설용지

용도	용적률(%이하)	최고층수(층이하)
	건폐율(%이하)	최저층수(층이상)

N


SCALE : 1/2,000

0 25 50 100(m)

서산테크노밸리 조성사업 지구단위계획

건축물 등에 관한 도시관리계획 결정도



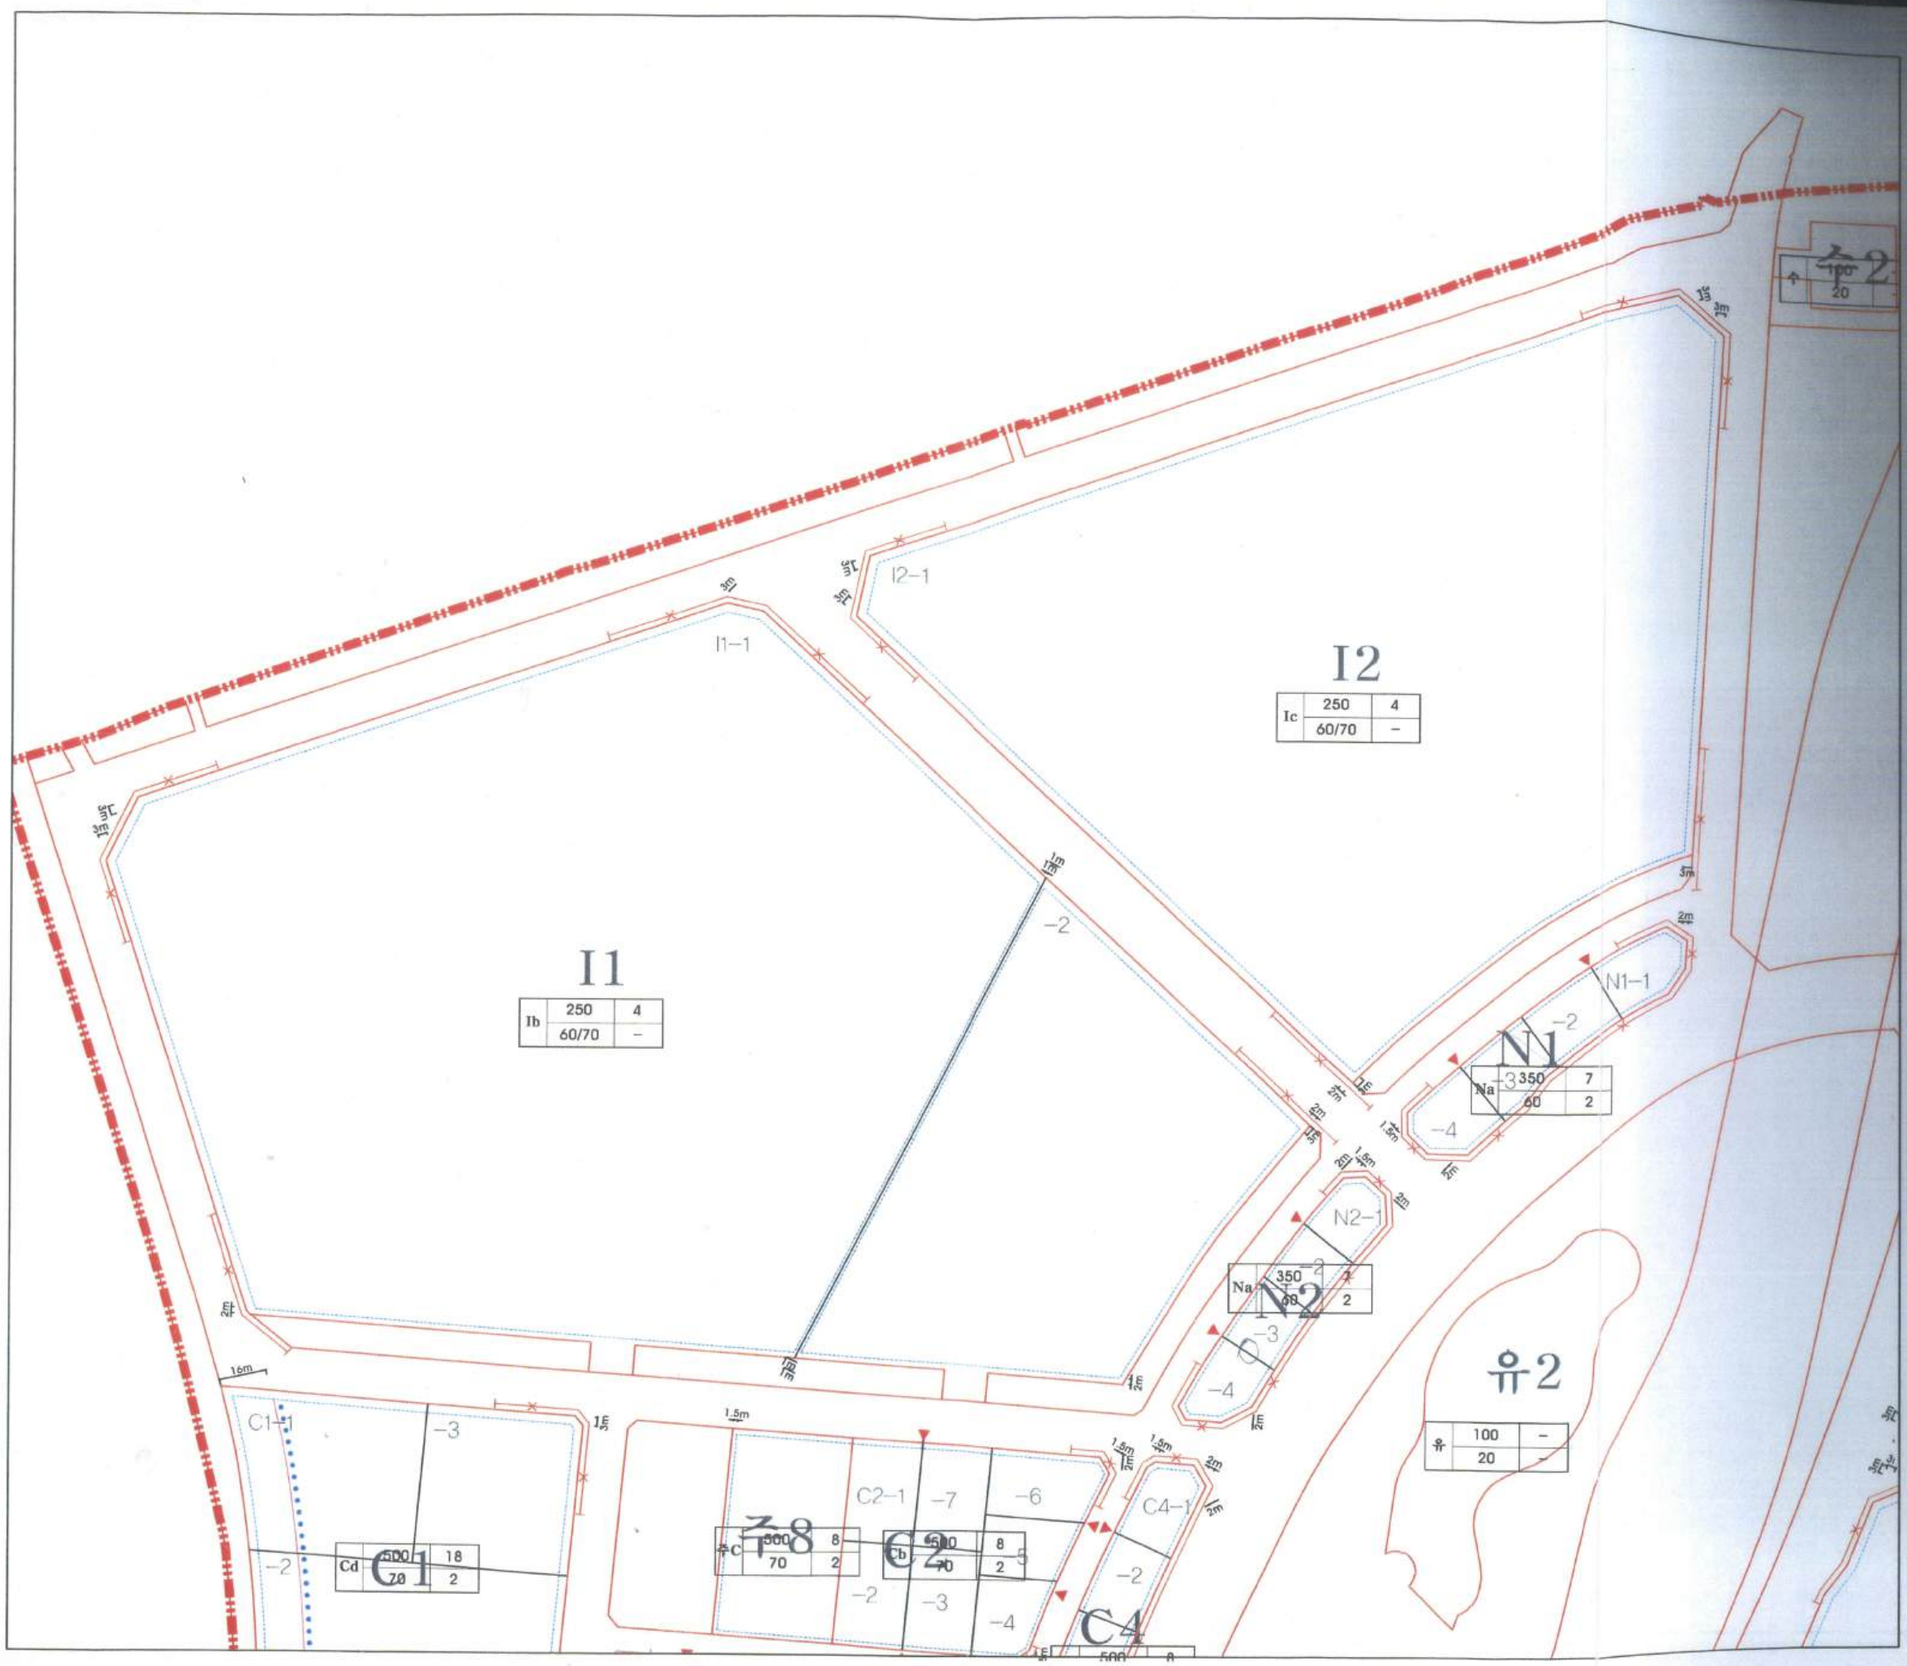

범 례

- 지구단위계획구역
- 획지경계선
- 대지분할가능선
- 건축한계선(m)
- 벽면한계선(m)(8층이상)
- 25층이하
- 20층이하
- 12층이하
- 차량출입구(권장)
- 주행방향
- 연도형상가(권장)
- 공라지표층(권장)
- 보행자전용도로
- 단지내 보행통로
- 공공보행통로
- 차량출입불허구간

※ 공동주택용지

용도	용적률(%이하) (기준/최대/상한)	최고층수(층이하) (평균층수(층이하))
	건폐율(%이하)	–

※ 산업시설용지

용도	용적률(%이하)	최고층수(층이하)
	건폐율(%이하) (기준/완화)	–

※ 기타시설용지

용도	용적률(%이하)	최고층수(층이하)
	건폐율(%이하)	최저층수(층이상)

N

SCALE : 1/2,000

0 25 50 100(m)

서산테크노밸리 조성사업 지구단위계획

건축물 등에 관한 도시관리계획 결정도





범 례

- 지구단위계획구역
- 획지경계선
- 대지분할가능선
- 건축한계선(m)
- 벽면한계선(m)(8층이상)
- 25층이하
- 20층이하
- 12층이하
- 차량출입구(권장)
- 주통방향
- 연도형상가(권장)
- 경관지표등(권장)
- 보행자전용도로
- 단지내 보행통로
- 공공보행통로
- 차량출입불허구간

※ 공동주택용지

용도	용적률(%이하) (기준/허용/상한)	최고층수(층이하) (평균층수(층이하))
	건폐율(%이하)	–

※ 산업시설용지

용도	용적률(%이하)	최고층수(층이하)
	건폐율(%이하) (기준/완화)	–

※ 기타시설용지

용도	용적률(%이하)	최고층수(층이하)
	건폐율(%이하)	최저층수(층이상)

N

SCALE : 1/3,000

0 25 50 150(m)

서산테크노밸리 조성사업 지구단위계획

건축물 등에 관한 도시관리계획 결정도



범 례

- 지구단위계획구역
- 획지경계선
- 대지분할가능선
- 건축한계선(m)
- 벽면한계선(m)(8층이상)
- 25층이하
- 20층이하
- 12층이하
- 차량출입구(권장)
- 주동방향
- 연도형상가(권장)
- 경관지표등(권장)
- 보행자전용도로
- 단지내 보행통로
- 공공보행통로
- 차량출입불허구간

※ 공동주택용지

용도	용적률(%이하) (기준/허용/상한)	최고층수(층이하) (평균층수(층이하))
	건폐율(%이하)	-

※ 산업시설용지

용도	용적률(%이하)	최고층수(층이하)
	건폐율(%이하) (기준/완화)	-

※ 기타시설용지

용도	용적률(%이하)	최고층수(층이하)
	건폐율(%이하)	최저층수(층이상)

N

SCALE : 1/3,000

0 25 50 150(m)

서산테크노밸리 조성사업 지구단위계획

건축물 등에 관한 도시관리계획 결정도



범 례

- 지구단위계획구역
- 획지경계선
- 대지분할가능선
- 건축한계선(m)
- 벽면한계선(m)(8층이상)
- 25층이하
- 20층이하
- 12층이하
- 차량출입구(권장)
- 주동방향
- 연도형상가(권장)
- 경관지표등(권장)
- 보행자전용도로
- 단지내 보행통로
- 공공보행통로
- 차량출입불허구간

※ 공동주택용지

용도	용적률(%이하) (기존/허용/상한)	최고층수(층이하) (평균층수(층이하))
	건폐율(%이하)	-

※ 산업시설용지

용도	용적률(%이하)	최고층수(층이하)
	건폐율(%이하) (기존/허용)	-

※ 기타시설용지

용도	용적률(%이하)	최고층수(층이하)
	건폐율(%이하)	최저층수(층이상)

N

SCALE : 1/3,000

0 25 50 150(m)

서산테크노밸리 조성사업 지구단위계획

건축물 등에 관한 도시관리계획 결정도



범 례

- 지구단위계획구역
- 획지경계선
- 대지분할가능선
- 건축한계선(m)
- 벽면한계선(m)(8층이상)
- 25층이하
- 20층이하
- 12층이하
- 차량출입구(권장)
- 주동방향
- 연도형상가(권장)
- 경관지표등(권장)
- 보행자전용도로
- 단지내 보행통로
- 공공보행통로
- 차량출입불허구간

※ 공동주택용지

용도	용적률(%이하) (기준/허용/상한)	최고층수(층이하) (평균층수(층이하))
	건폐율(%이하)	-

※ 산업시설용지

용도	용적률(%이하)	최고층수(층이하)
	건폐율(%이하) (기준/완화)	-

※ 기타시설용지

용도	용적률(%이하)	최고층수(층이하)
	건폐율(%이하)	최저층수(층이상)

N

SCALE : 1/2,000

0 25 50 100(m)