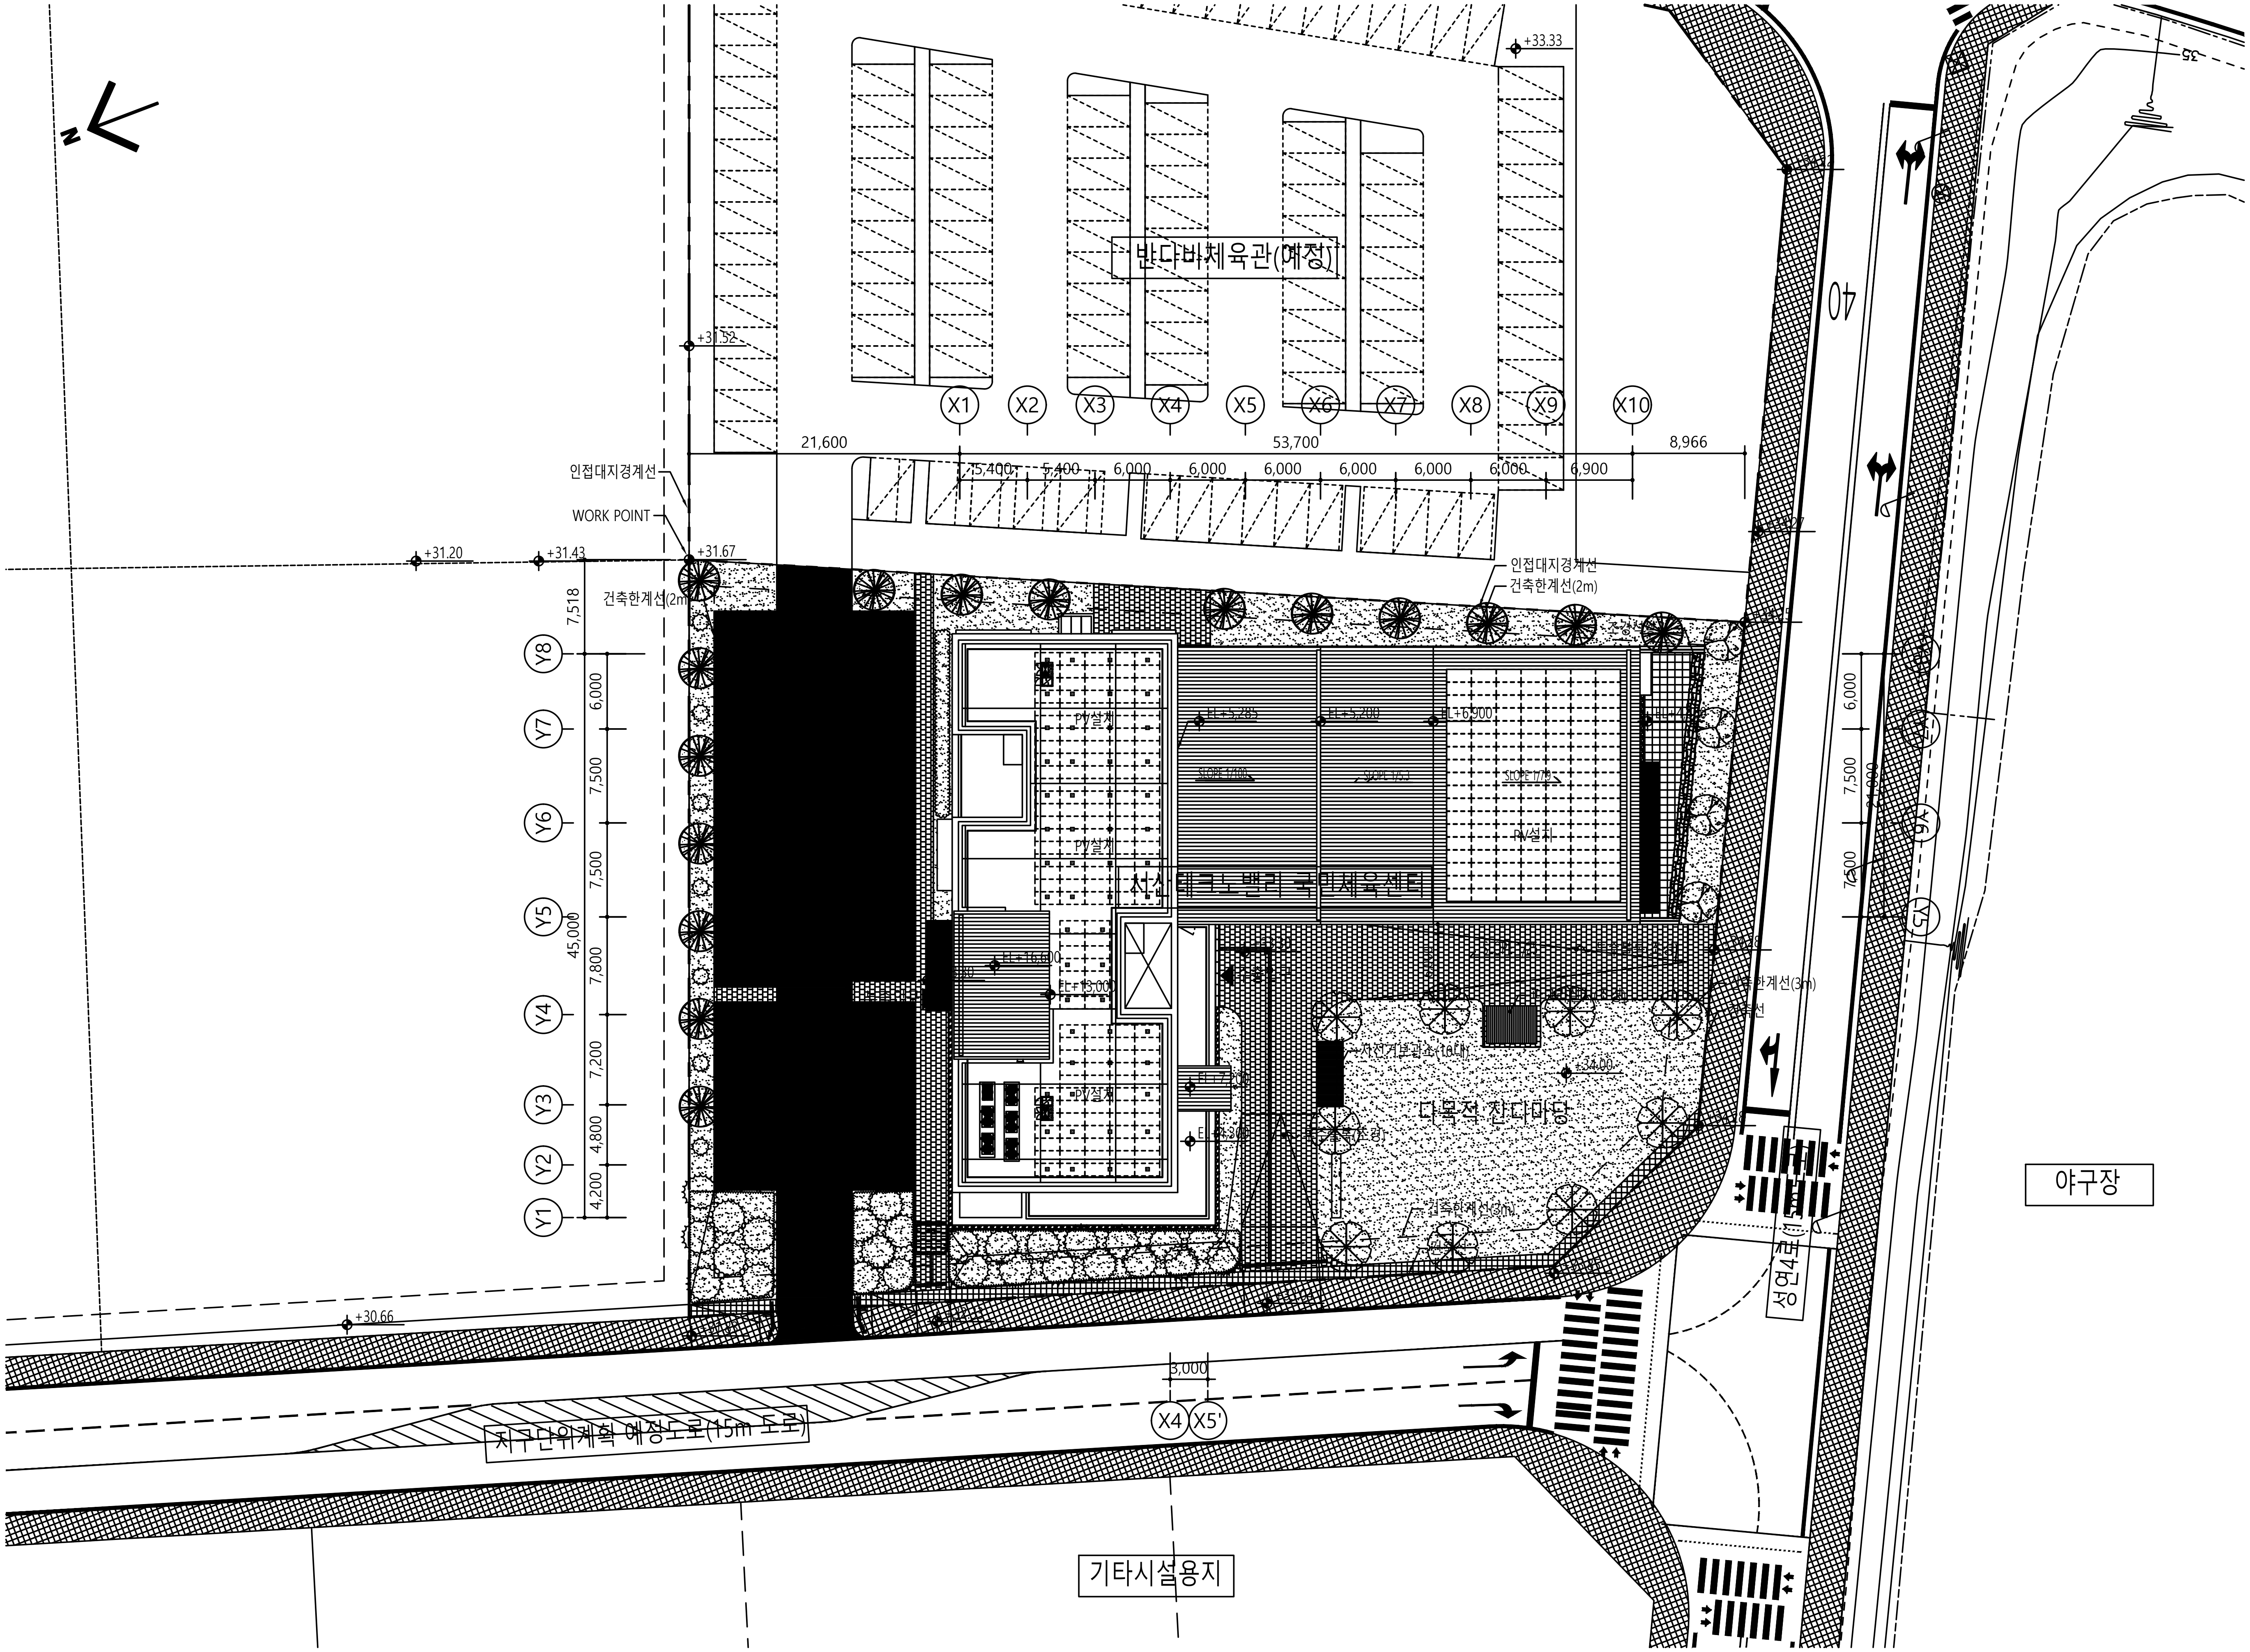
반다비체육관(예정)
서산테크노밸리 국민체육센터
다목적 잔디마당
야구장
기타시설용지
지구단위계획 예정도로(15m 도로)
인접대지경계선
WORK POINT
건축한계선(2m)
건축한계선(3m)
자전거보관소(10대)
PV설치
SLOPE 1/100
SLOPE 1/5.3
SLOPE 1/7.9
EL+5,285
EL+5,200
EL+6,900
EL+16,600
EL+13,000
EL+7,200
EL+4,300
+33.33
+31.52
+31.67
+31.43
+31.20
+30.66
+34.00
X1
X2
X3
X4
X5
X6
X7
X8
X9
X10
X4
X5'
Y1
Y2
Y3
Y4
Y5
Y6
Y7
Y8
21,600
53,700
8,966
5,400
5,400
6,000
6,000
6,000
6,000
6,000
6,000
6,900
7,518
6,000
7,500
7,500
7,800
7,200
4,800
4,200
45,000
3,000
40

1. 건축레벨
1F F.L=E.L=GL+33.30
기계실 F.L=EL-6,000
전기실 F.L=EL-5,600
B1 F.L=EL-6,000
1F F.L=EL±0
2F F.L=EL+4,300
3F F.L=EL+8,600
RF1 F.L=EL+13,000
RF2 F.L=EL+16,600